


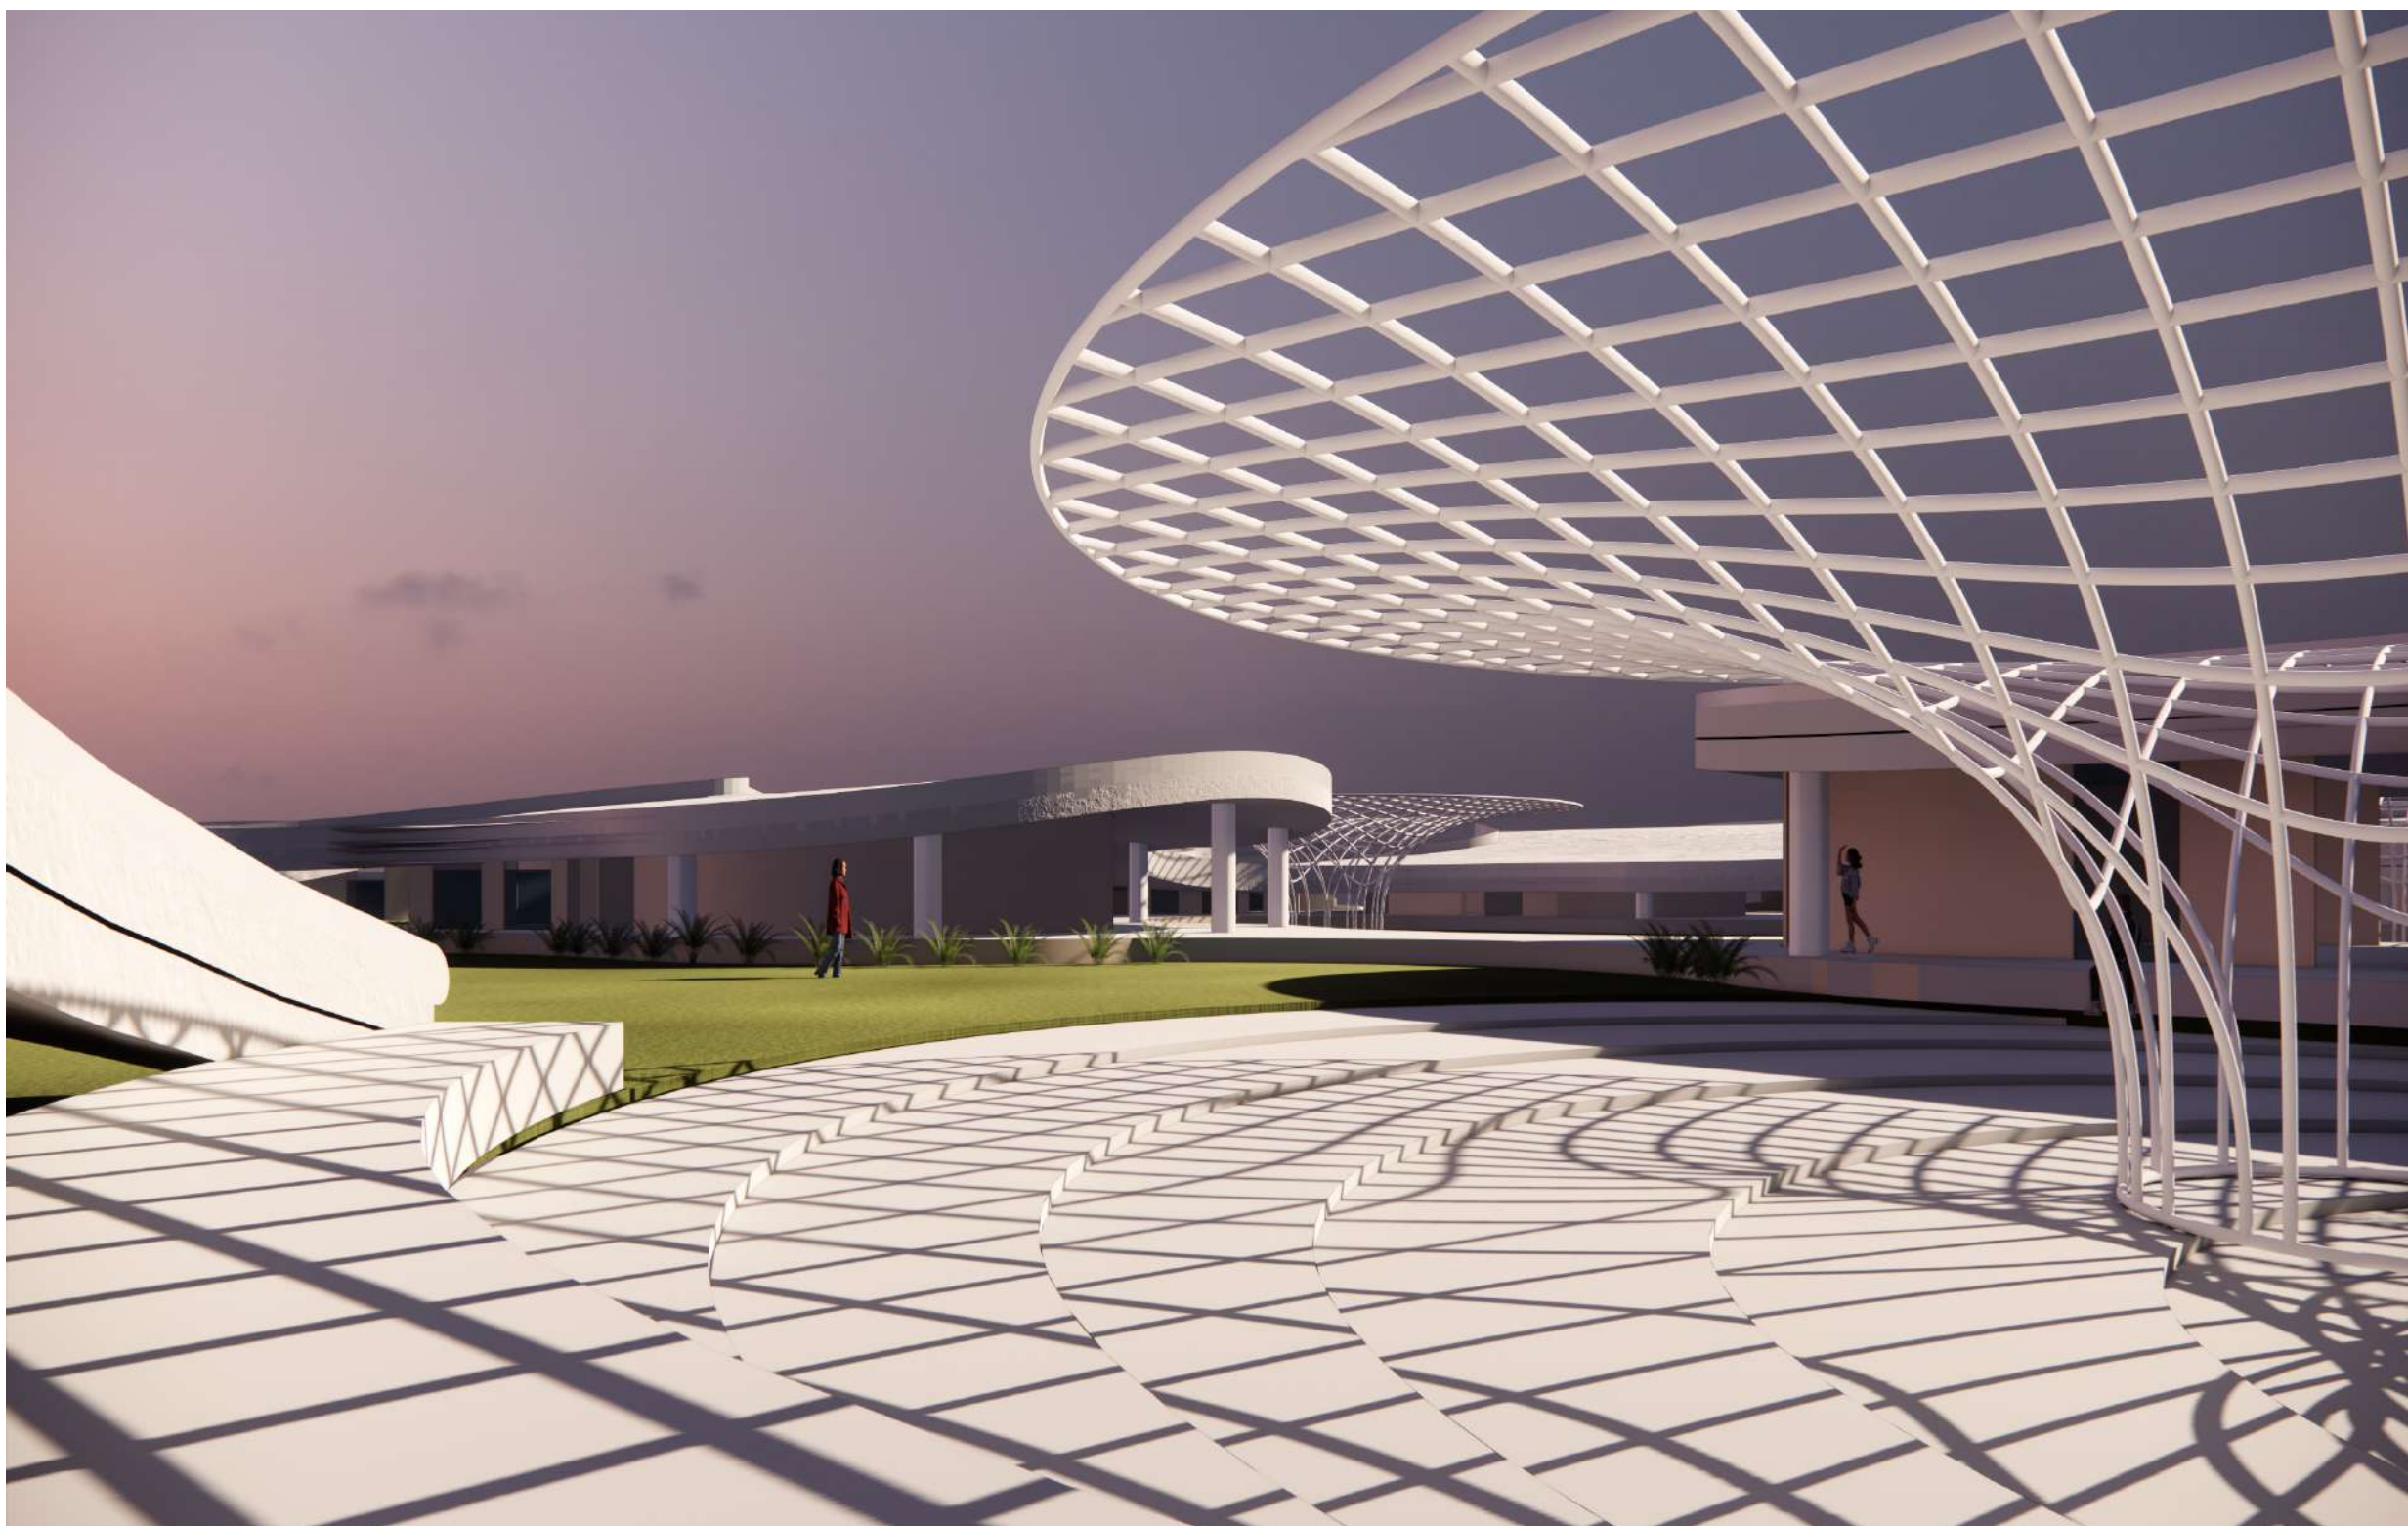

ARCHITECTURAL PORTFOLIO | 2026-27

ASAD MEMON

PersonalBrief



ASAD MEMON

Contact Information

Siddhpur, Patan, Gujarat
+91 8490-807258
memonasad011@gmail.com
@voidandvolume011
linkedin.com/in/asad-memon

Summary

I am architecture student with academic foundation, having completed a Diploma in Architecture. My education has provided me with a balanced understanding of architectural theory, construction technology, and practical design application. I am passionate about designing meaningful spaces for living beings that integrate functionality, comfort, and aesthetics. I have hands-on experience in architectural drawings, space planning, form development, and visualization through academic projects.

Education

- Parul Institute of Architecture & Research, Vadodara, Gujarat
Bachelor In Architecture
2023-2028
- Parul Institute of Architecture & Research, Vadodara, Gujarat
Diploma In Architecture
2020-2023
- Gokul Global School , Siddhpur, Patan, Gujarat
Secondary School
2015-2020

Software skills



Autocad

●●●●●○



Sketch up

●●●●○○



Rhino3D

●●●○○○



Revit

●○○○○○



Enscape

●●●●○○




Lumion

●●●●○○



Twinmotion

●●○○○○

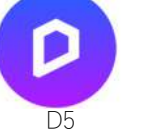

D5

●○○○○○



Photoshop


●●●○○○



InDesign

●●○○○○

Hobbies

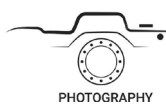

Projects

- The Flow Forum- Institutional Design
- Bandhani घर
- Luminous Veil House
- Sukoongruh
- COA Architectural Heritage 2025
- Freelancing

Participations

- COA Architectural Heritage 2024
- COA Architectural Heritage 2025
- Tiny House 2024
- University Design ANAND (gov. project)
- University Design AMRAVATI (approved gov. project)

Language

- ENGLISH
- HINDI
- GUJARATI
- URDU

C O N T E N T S

01. THE FLOW FORUM



02. BANDHANI



03. LUMINOUS VEIL HOUSE



04. SUKOOONGRUH



05. HERITAGE DOCUMENTATION



06. FREELANCING




01






01

THE FLOW FORUM INSTITUTIONAL DESIGN

This project have circular organic campus layout where repeating round modules form academic blocks, courtyards, and fluid movement paths. A central plaza anchors the plan and organizes circulation on all sides. The sections show tree-like canopy structures used to create shaded walkways, reflecting a climate-responsive approach for Anand's heat. The exploded axonometric breaks the project into roof form, internal functional layout, and the landscaped ground zone, clarifying how the flowing geometry shapes both built and open spaces. Rendered views at the bottom illustrate active courtyards, shaded social areas, and a pedestrian-friendly environment that supports interaction across the campus.

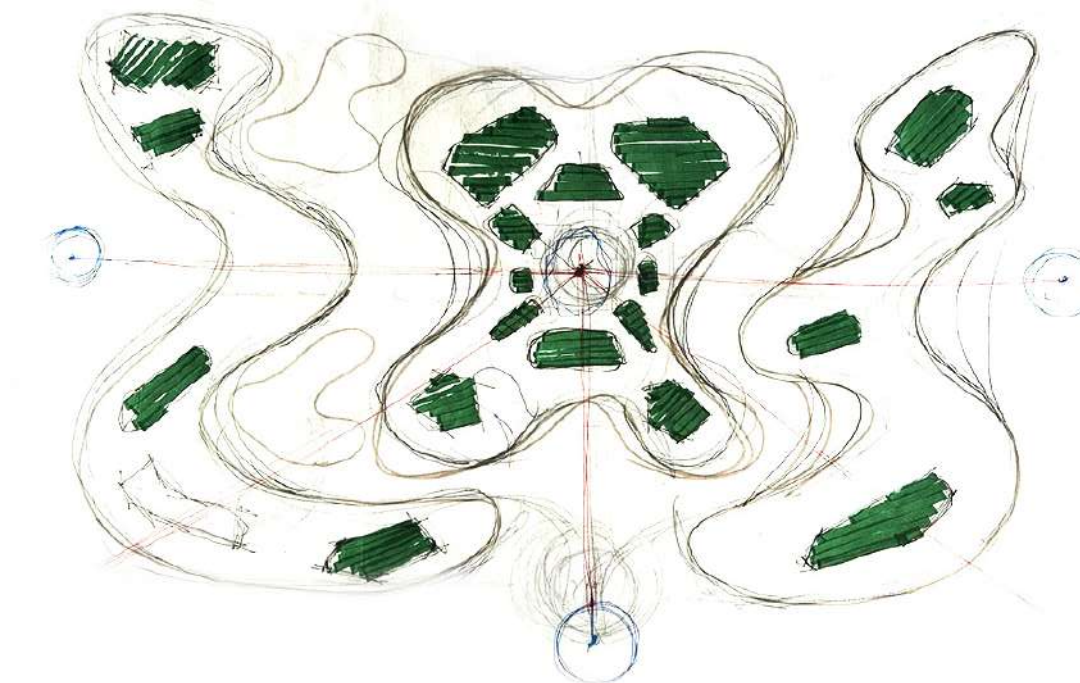

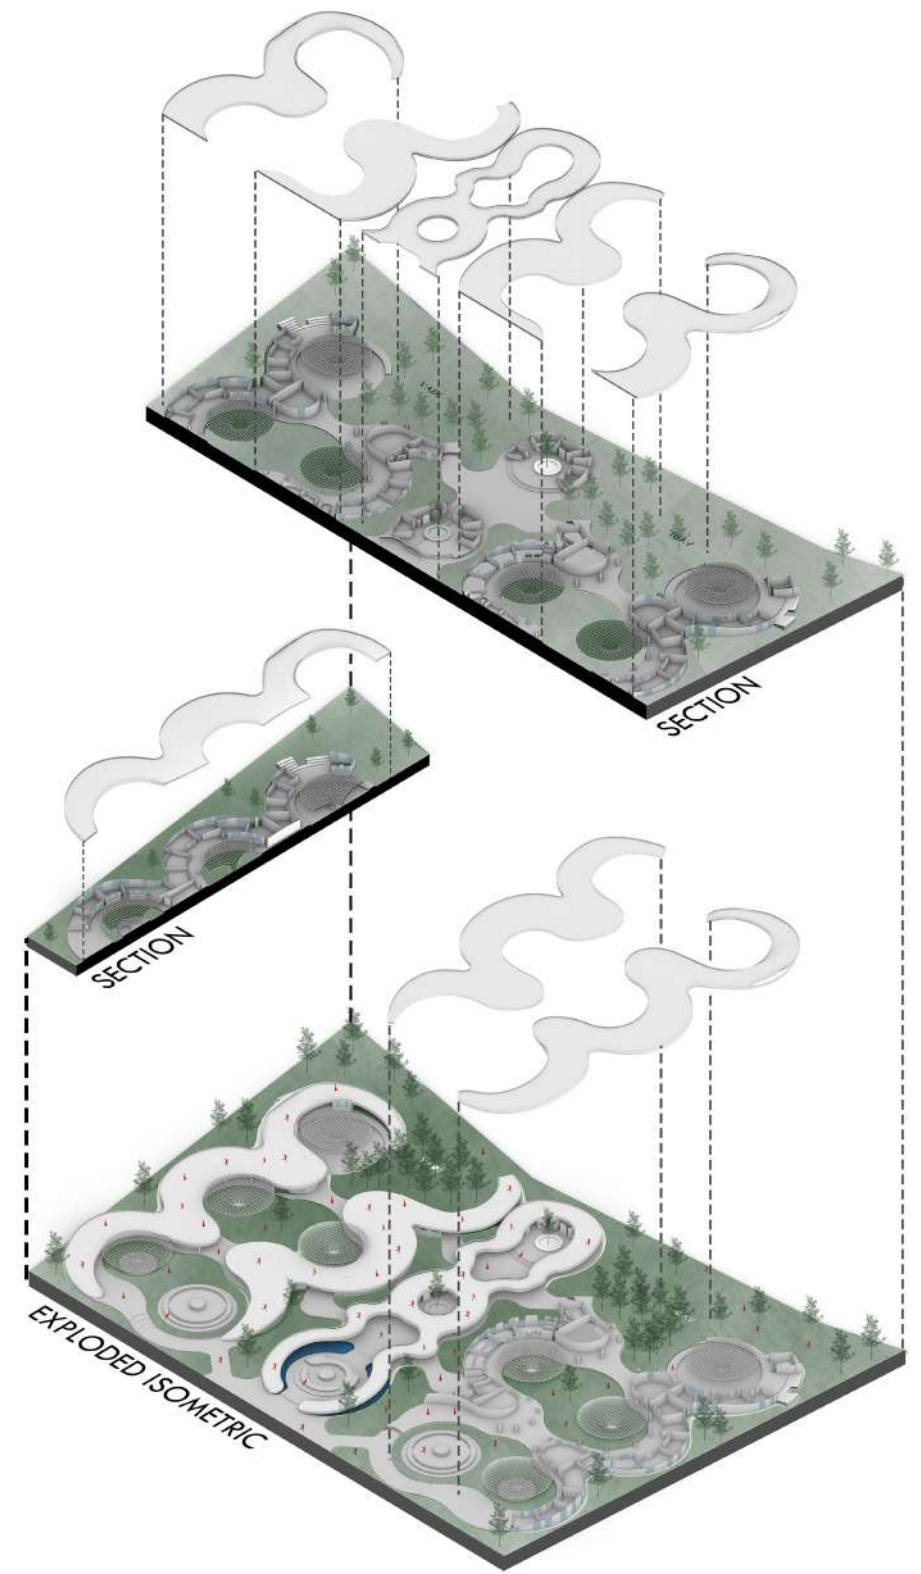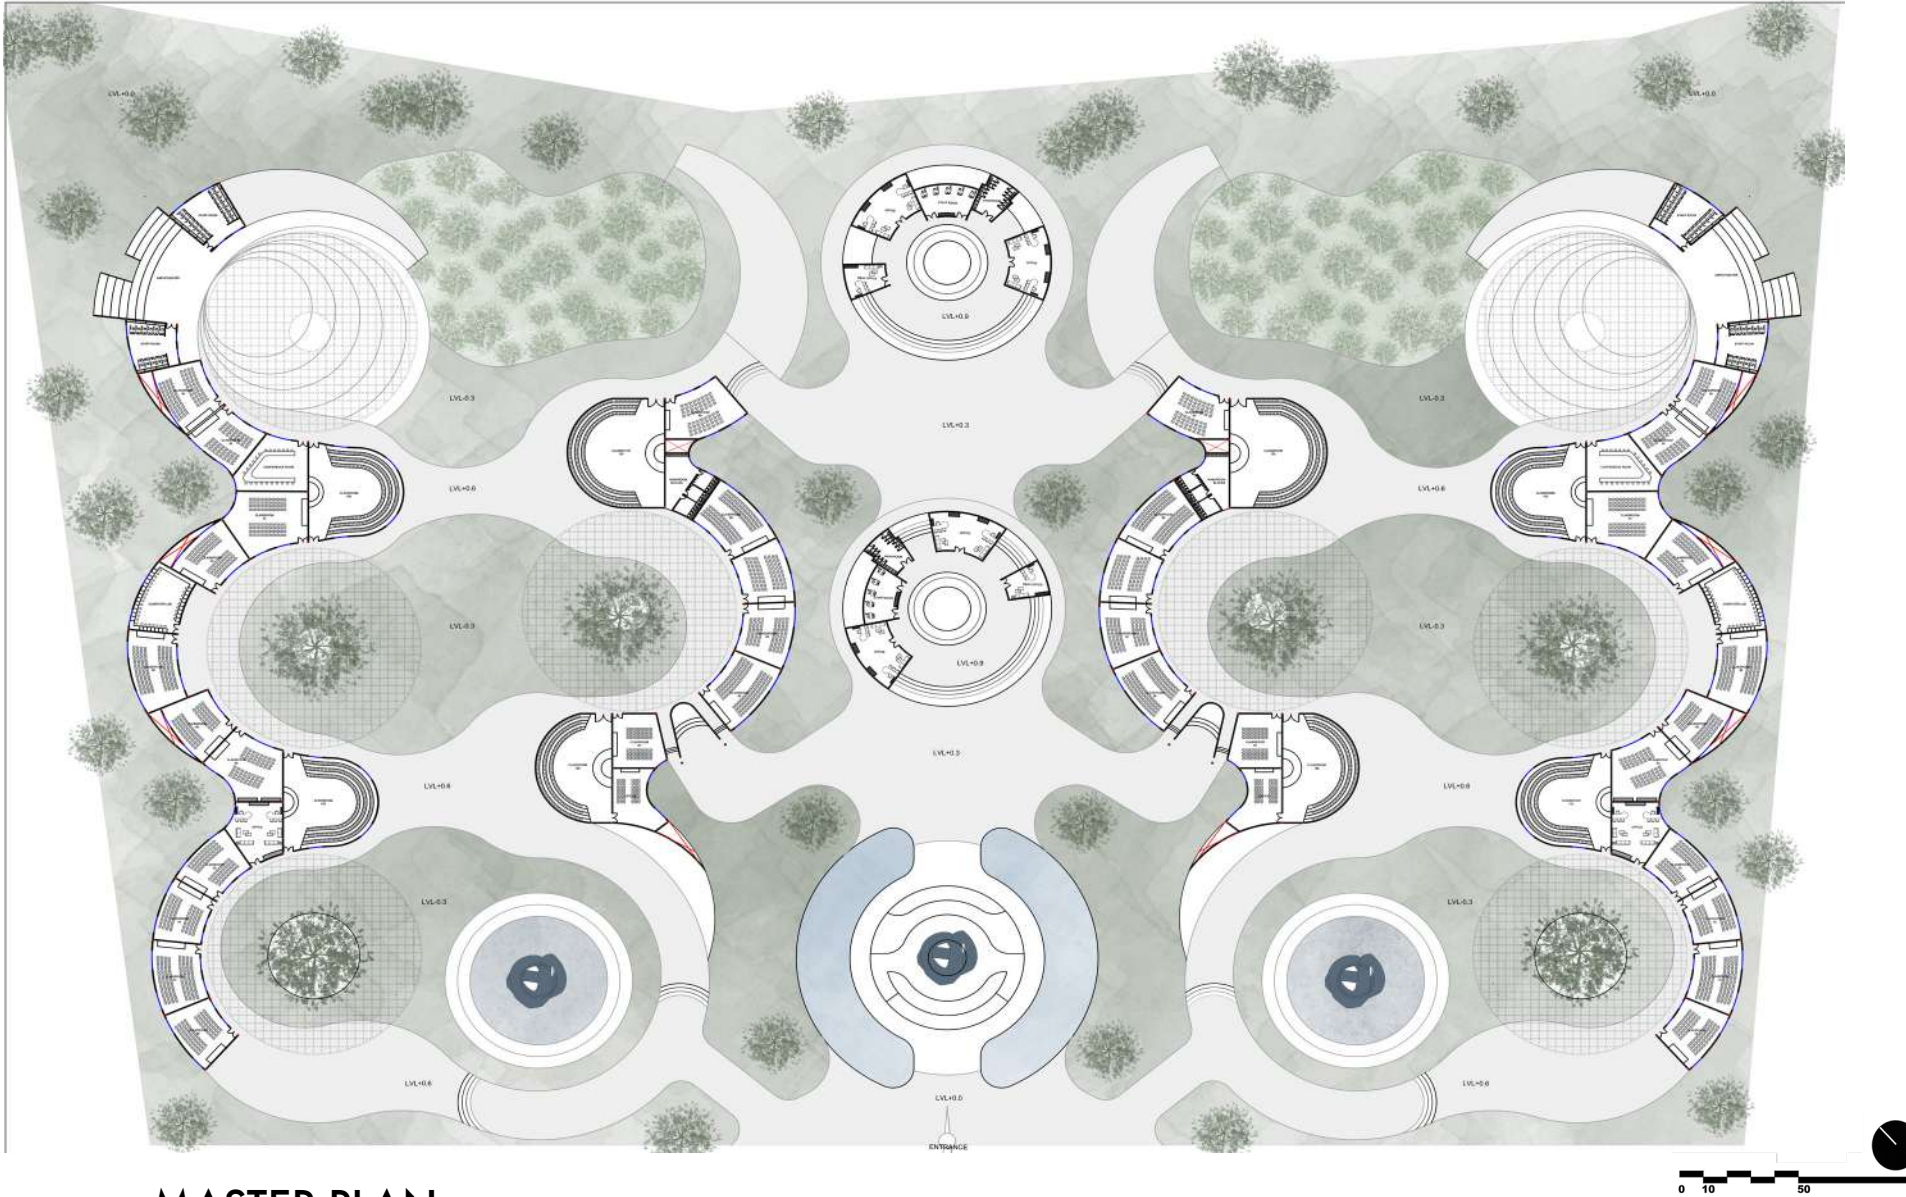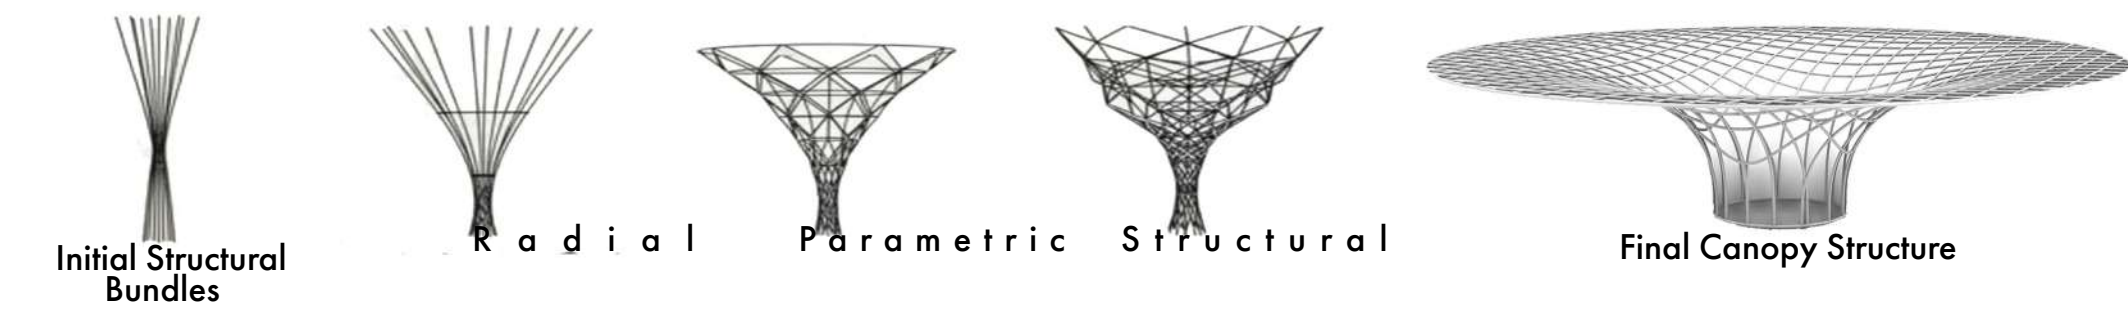

PERSPECTIVE ILLUSTRATING ROOFTOP CIRCULATION




SHOWING THE BUILDING'S FLOW AROUND THE COLUMN



ELEVATED VIEW CAPTURED FROM THE ROOF




AERIAL VIEW HIGHLIGHTED THE BUILDING'S MOVEMENT

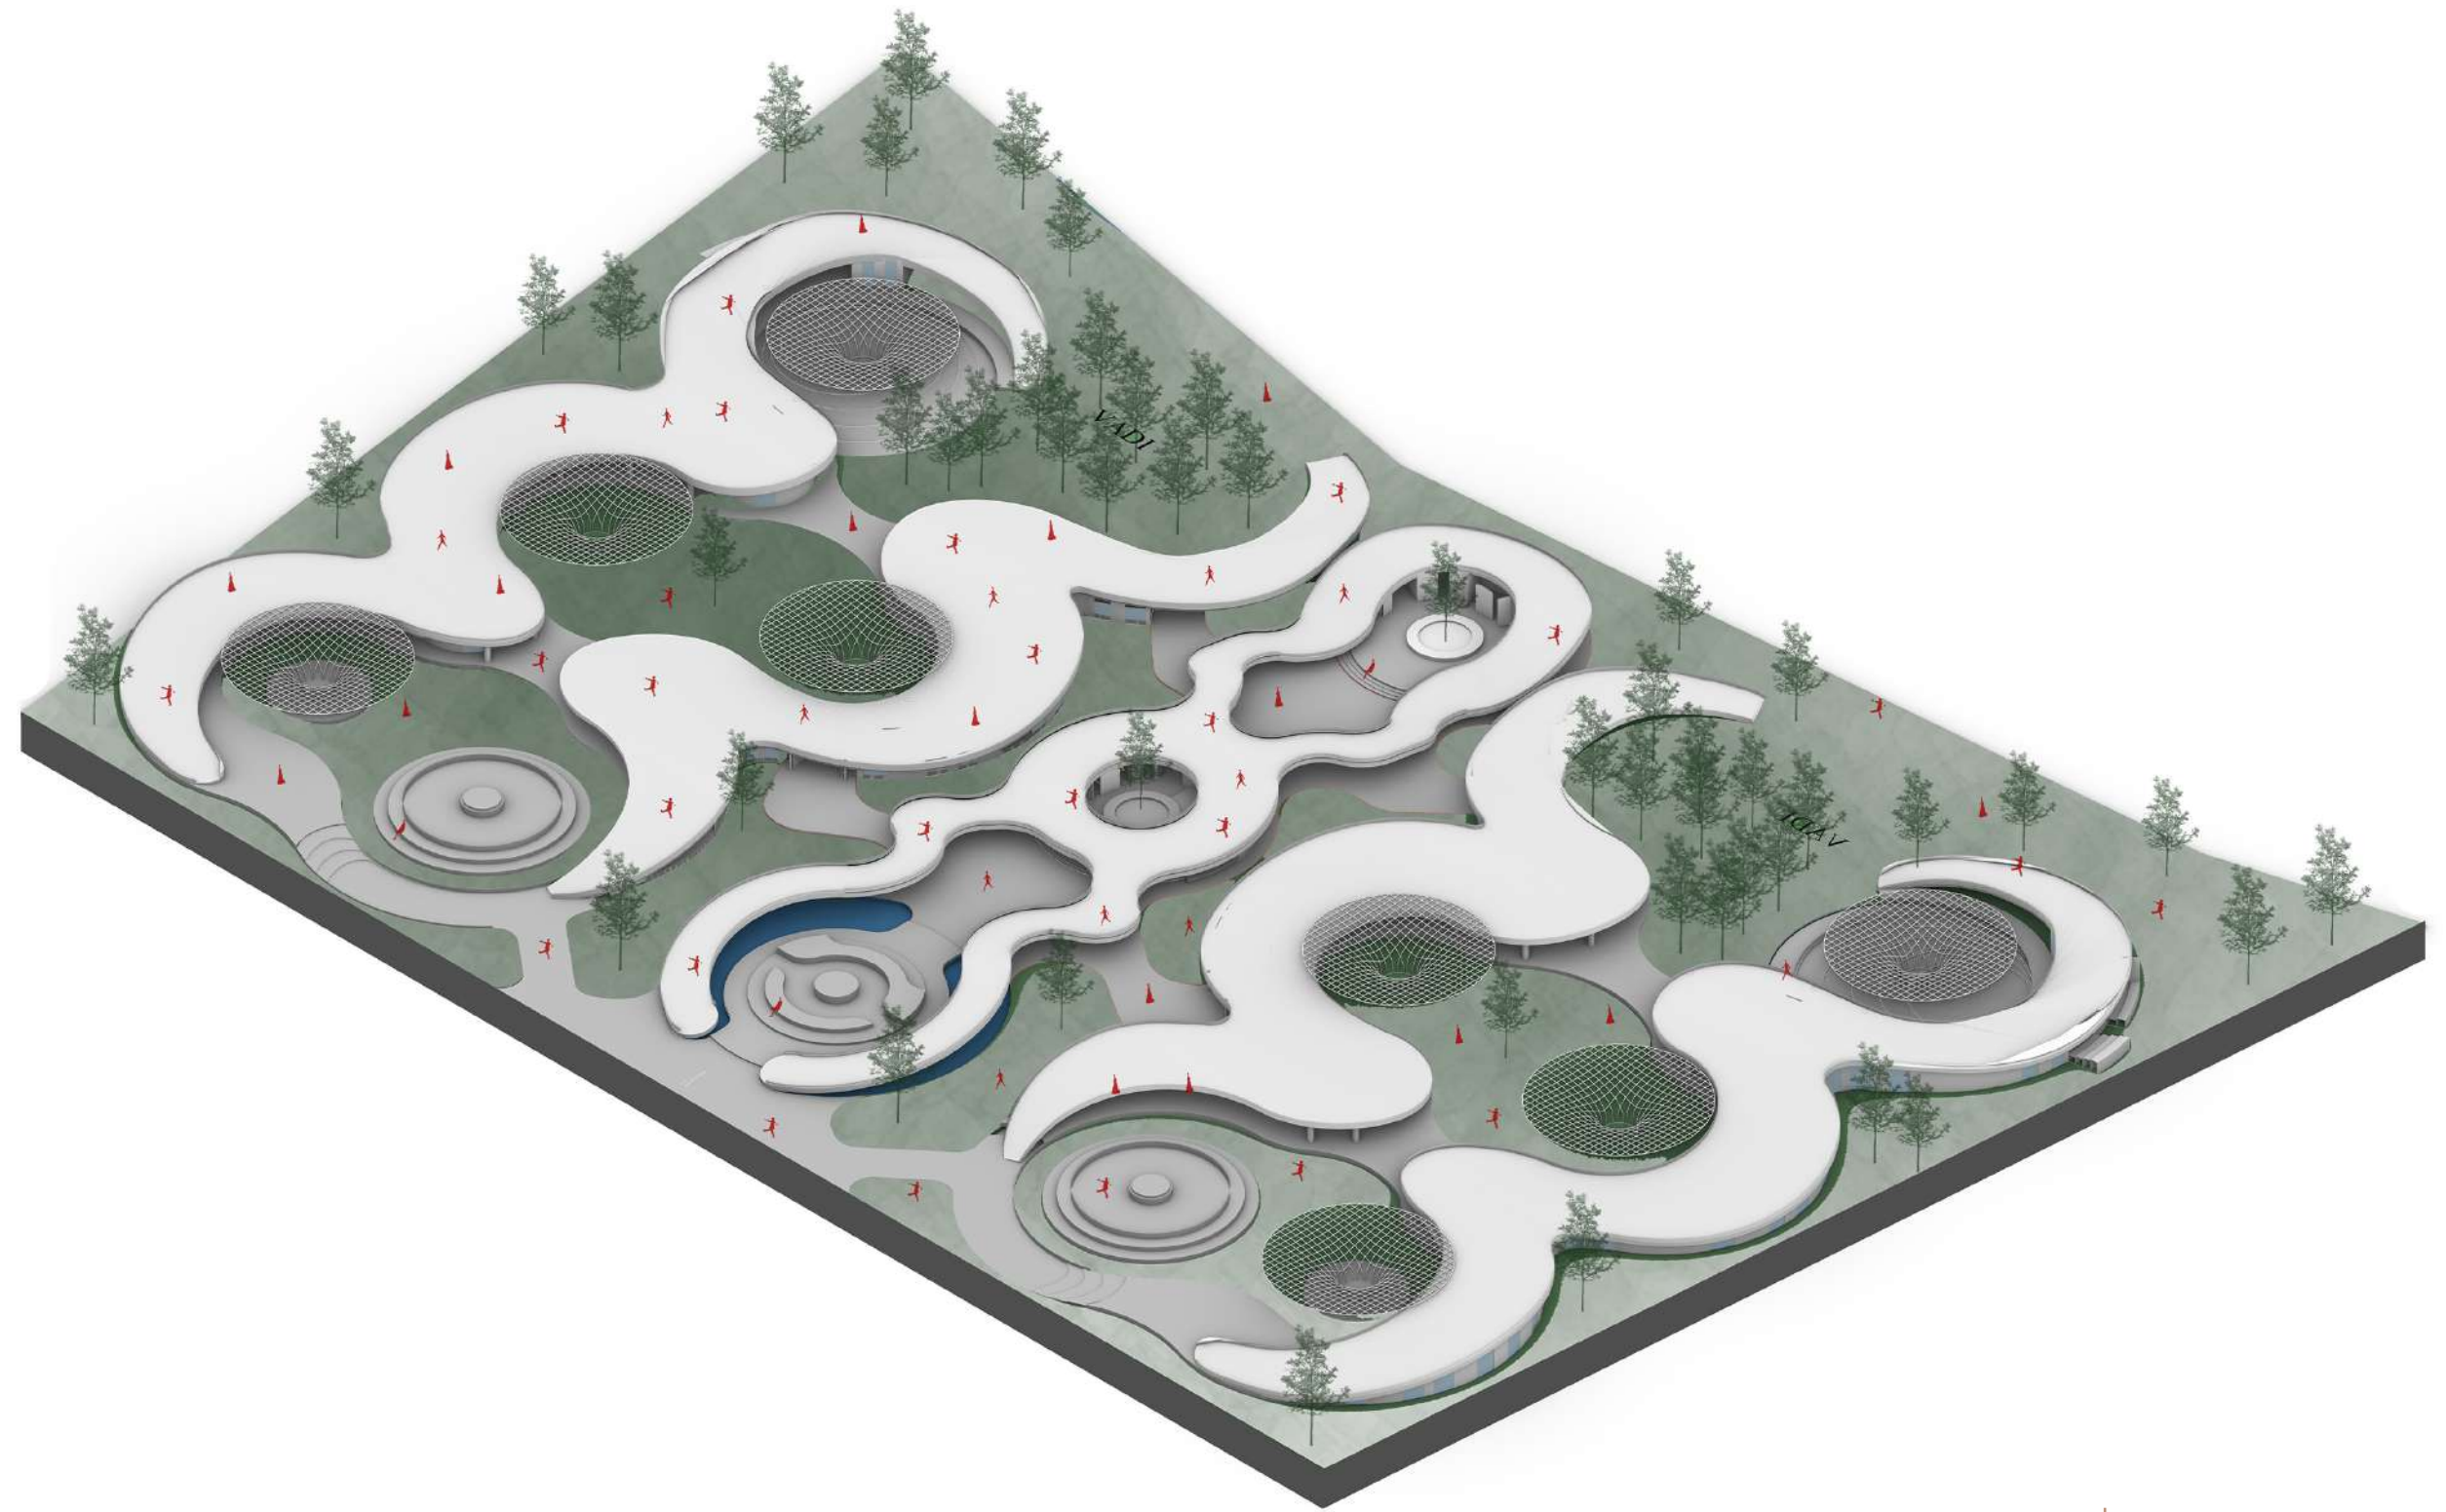




02 BANDHANI घर WORKSHOP DESIGN

The design of this Bandhani workshop embraces the concept of arcs, symbolizing the seamless flow of tradition and craftsmanship. The curved layout creates a harmonious connection between various functional zones: the tying area, dyeing area, wash area, and drying area. These elements are all organized to follow a natural, arc-like flow, optimizing space and enhancing efficiency while maintaining the artistry of the craft. The exhibition area, with its sweeping design, is the centerpiece, showcasing the beauty of Bandhani through an open, welcoming space. Behind the workshop, four dwellings for workers provide a sense of continuity and comfort, echoing the flow of the entire workshop. This design honors both the cultural heritage of Bandhani and the fluid nature of its creative process.

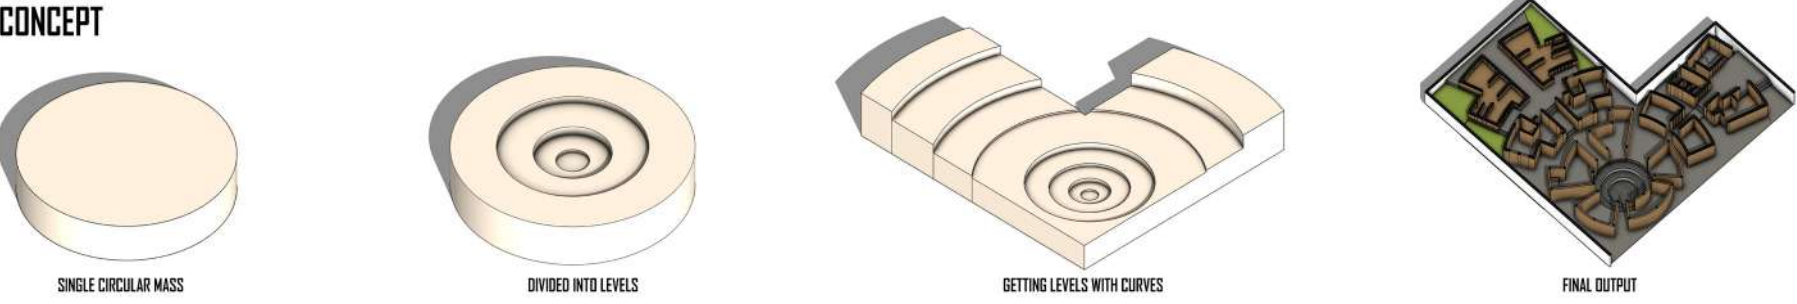

MASTER PLAN

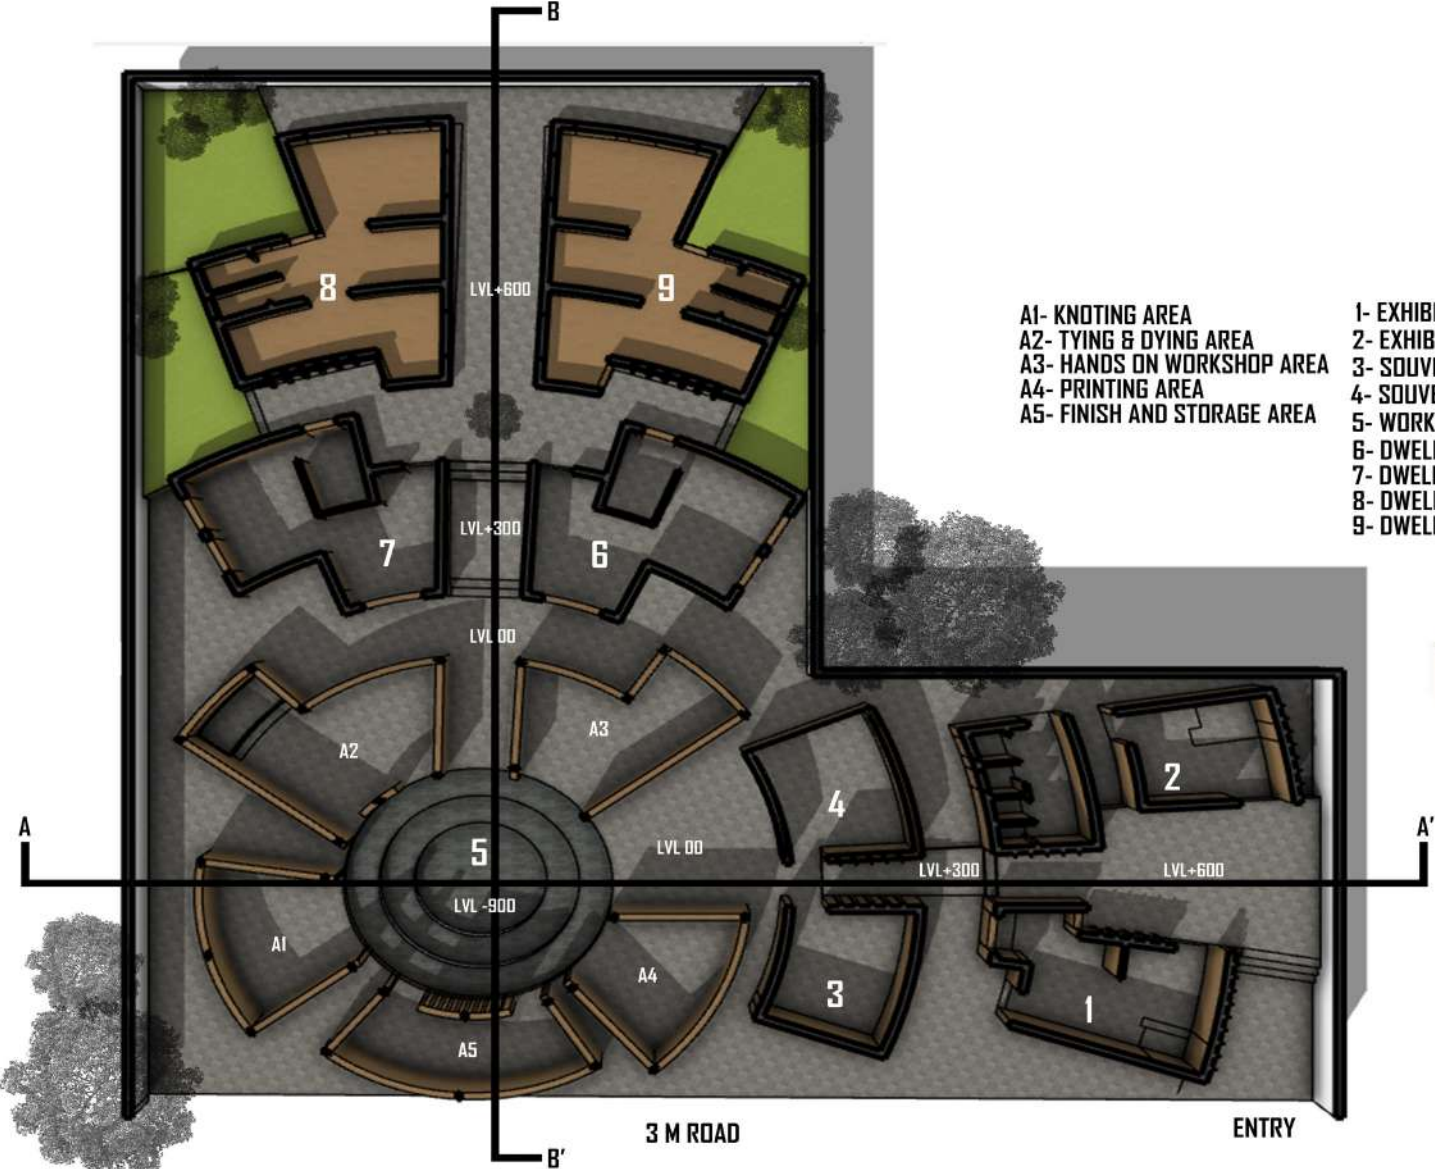

SECTION A-A'

SECTION B-B'






03

03 LUMINOUS VEIL HOUSE RESIDENTIAL DESIGN

Luminous Veil House explores the relationship between light, privacy, and everyday living within a compact residential setting. The design is organized around a central courtyard that acts as the heart of the house, allowing natural light and ventilation to flow through the interior spaces while creating a calm and intimate environment.

The spatial layout carefully arranges essential functions such as the workspace, pantry, toilet, and sitting areas around this courtyard, ensuring visual connectivity and environmental comfort. Semi-covered sitting spaces and an otla create transitional zones between indoor and outdoor areas, encouraging informal interaction and everyday activities.

CONCEPT DEVELOPMENT

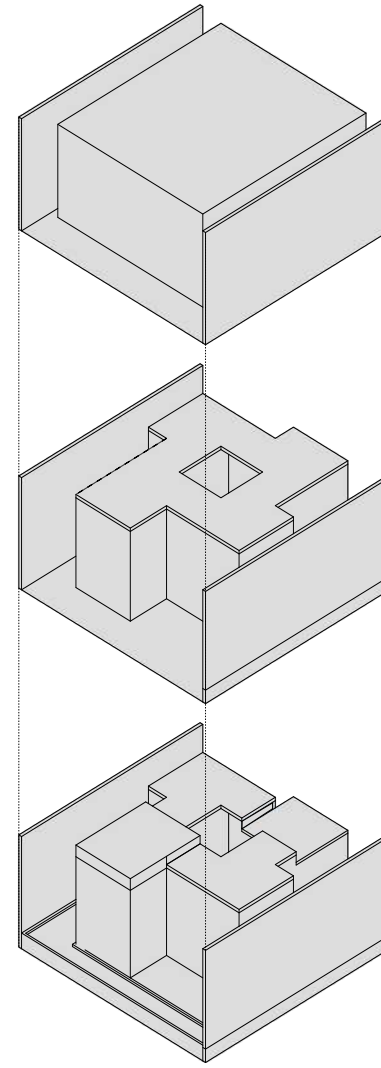

OPEN SITTING /SEMI COVER SPACE

GREEN SPACE AS BARRIER FOR PRIVACY

EXISTING WALL

EXISTING WALL

PARKING AREA

BUILD MASS

OTTA

3.0 MT WIDE ROAD

3.0 MT WIDE ROAD

PLAN

ROOF PLAN

FINAL MODEL

PLUMBING DETAIL MODEL

SECTION - SHOWING CHAMBERS

SECTION - CUT FROM WALL TO SHOW PLINTH

SECTION- CUT AT WINDOW MID

ROOF TOP VIEW


SECTION - SHOWING CHAMBERS WITH WATER TANK AND PIPES

SECTION - CUT FROM WALL TO SHOW PLINTH WITH WATER TANK AND PIPES

SECTION- CUT AT WINDOW MID WITH WATER TANK AND PIPES

ROOF TOP VIEW WITH WATER TANK AND PIPES



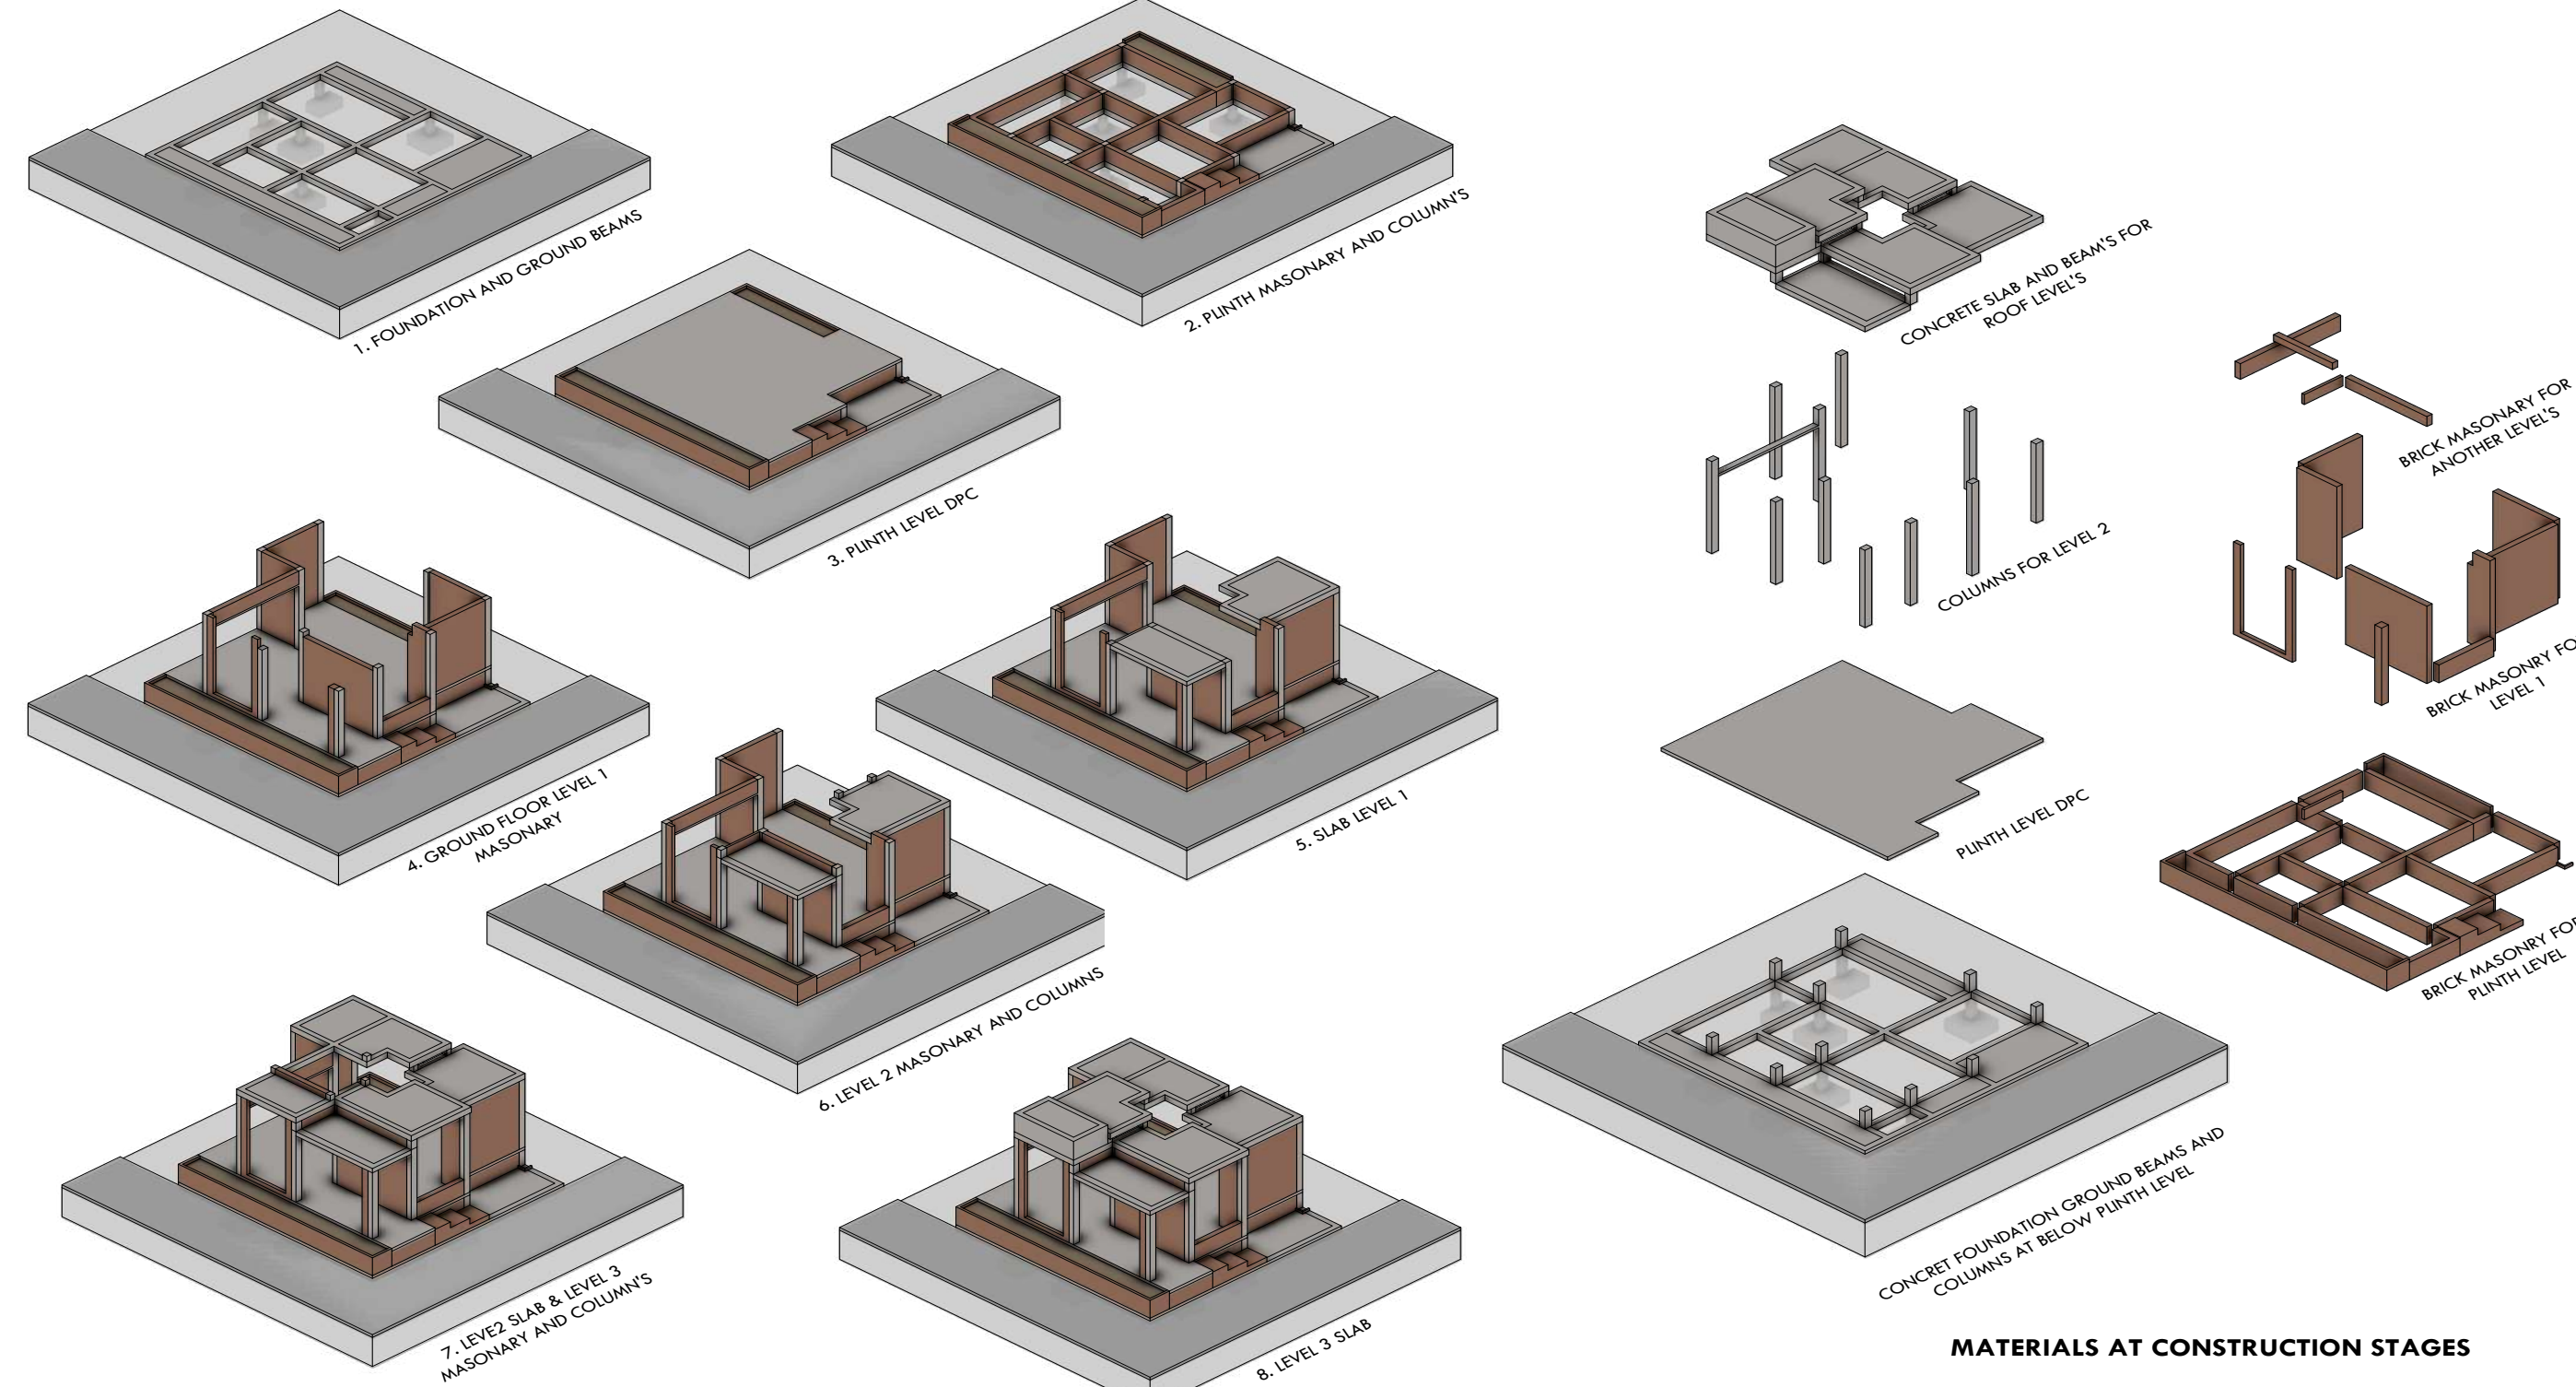

1. FOUNDATION AND GROUND BEAMS

2. PLINTH MASONRY AND COLUMNS

3. PLINTH LEVEL DPC

4. GROUND FLOOR LEVEL 1 MASONRY

5. SLAB LEVEL 1

6. LEVEL 2 MASONRY AND COLUMNS

7. LEVEL 2 SLAB & LEVEL 3 MASONRY AND COLUMNS

8. LEVEL 3 SLAB

CONCRETE SLAB AND BEAMS FOR ROOF LEVELS

COLUMNS FOR LEVEL 2

PLINTH LEVEL DPC

CONCRETE FOUNDATION GROUND BEAMS AND COLUMNS AT BELOW PLINTH LEVEL

BRICK MASONRY FOR ANOTHER LEVEL'S

BRICK MASONRY FOR LEVEL 1

BRICK MASONRY FOR PLINTH LEVEL

LEVELWISE CONSTRUCTION STAGES


MATERIALS AT CONSTRUCTION STAGES







04


04 TINY HOUSE 2024 SUKOONGRUH

The sheet presents a circular, organic campus layout where repeating round modules form academic blocks, courtyards, and fluid movement paths. A central plaza anchors the plan and organizes circulation on all sides. The sections show tree-like canopy structures used to create shaded walkways, reflecting a climate-responsive approach for Anand’s heat. The exploded axonometric breaks the project into roof form, internal functional layout, and the landscaped ground zone, clarifying how the flowing geometry shapes both built and open spaces. Rendered views at the bottom illustrate active courtyards, shaded social areas, and a pedestrian-friendly environment that supports interaction across the campus.

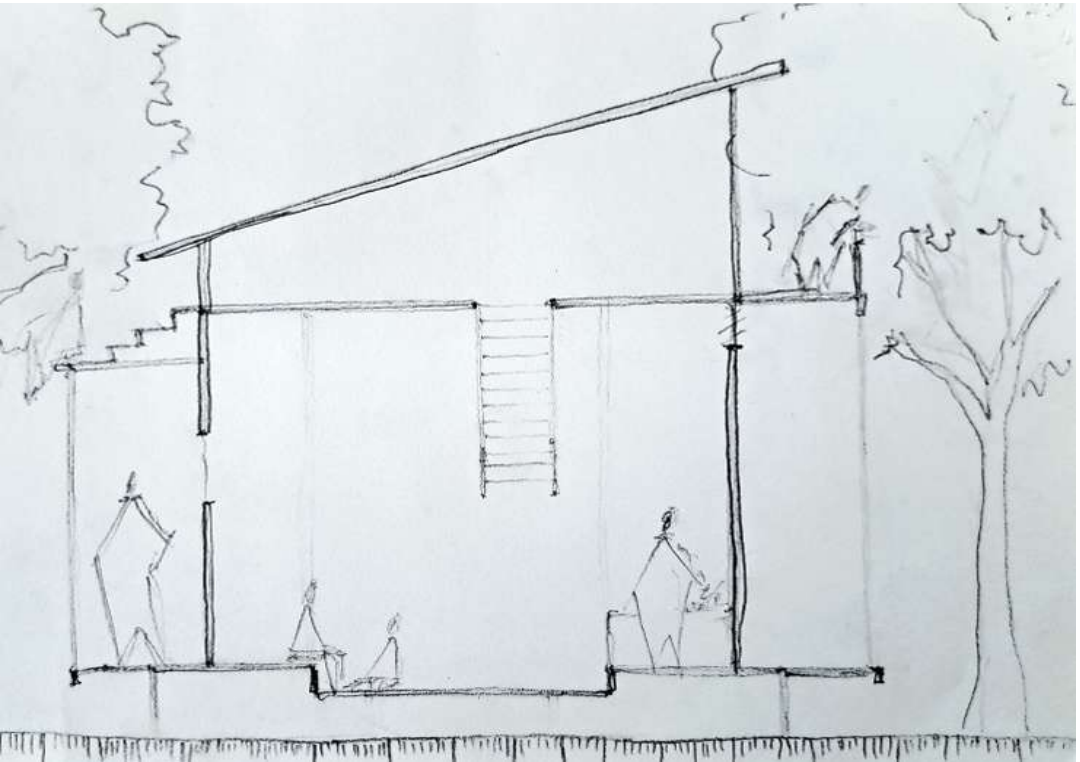

CONCEPTUAL DIAGRAM

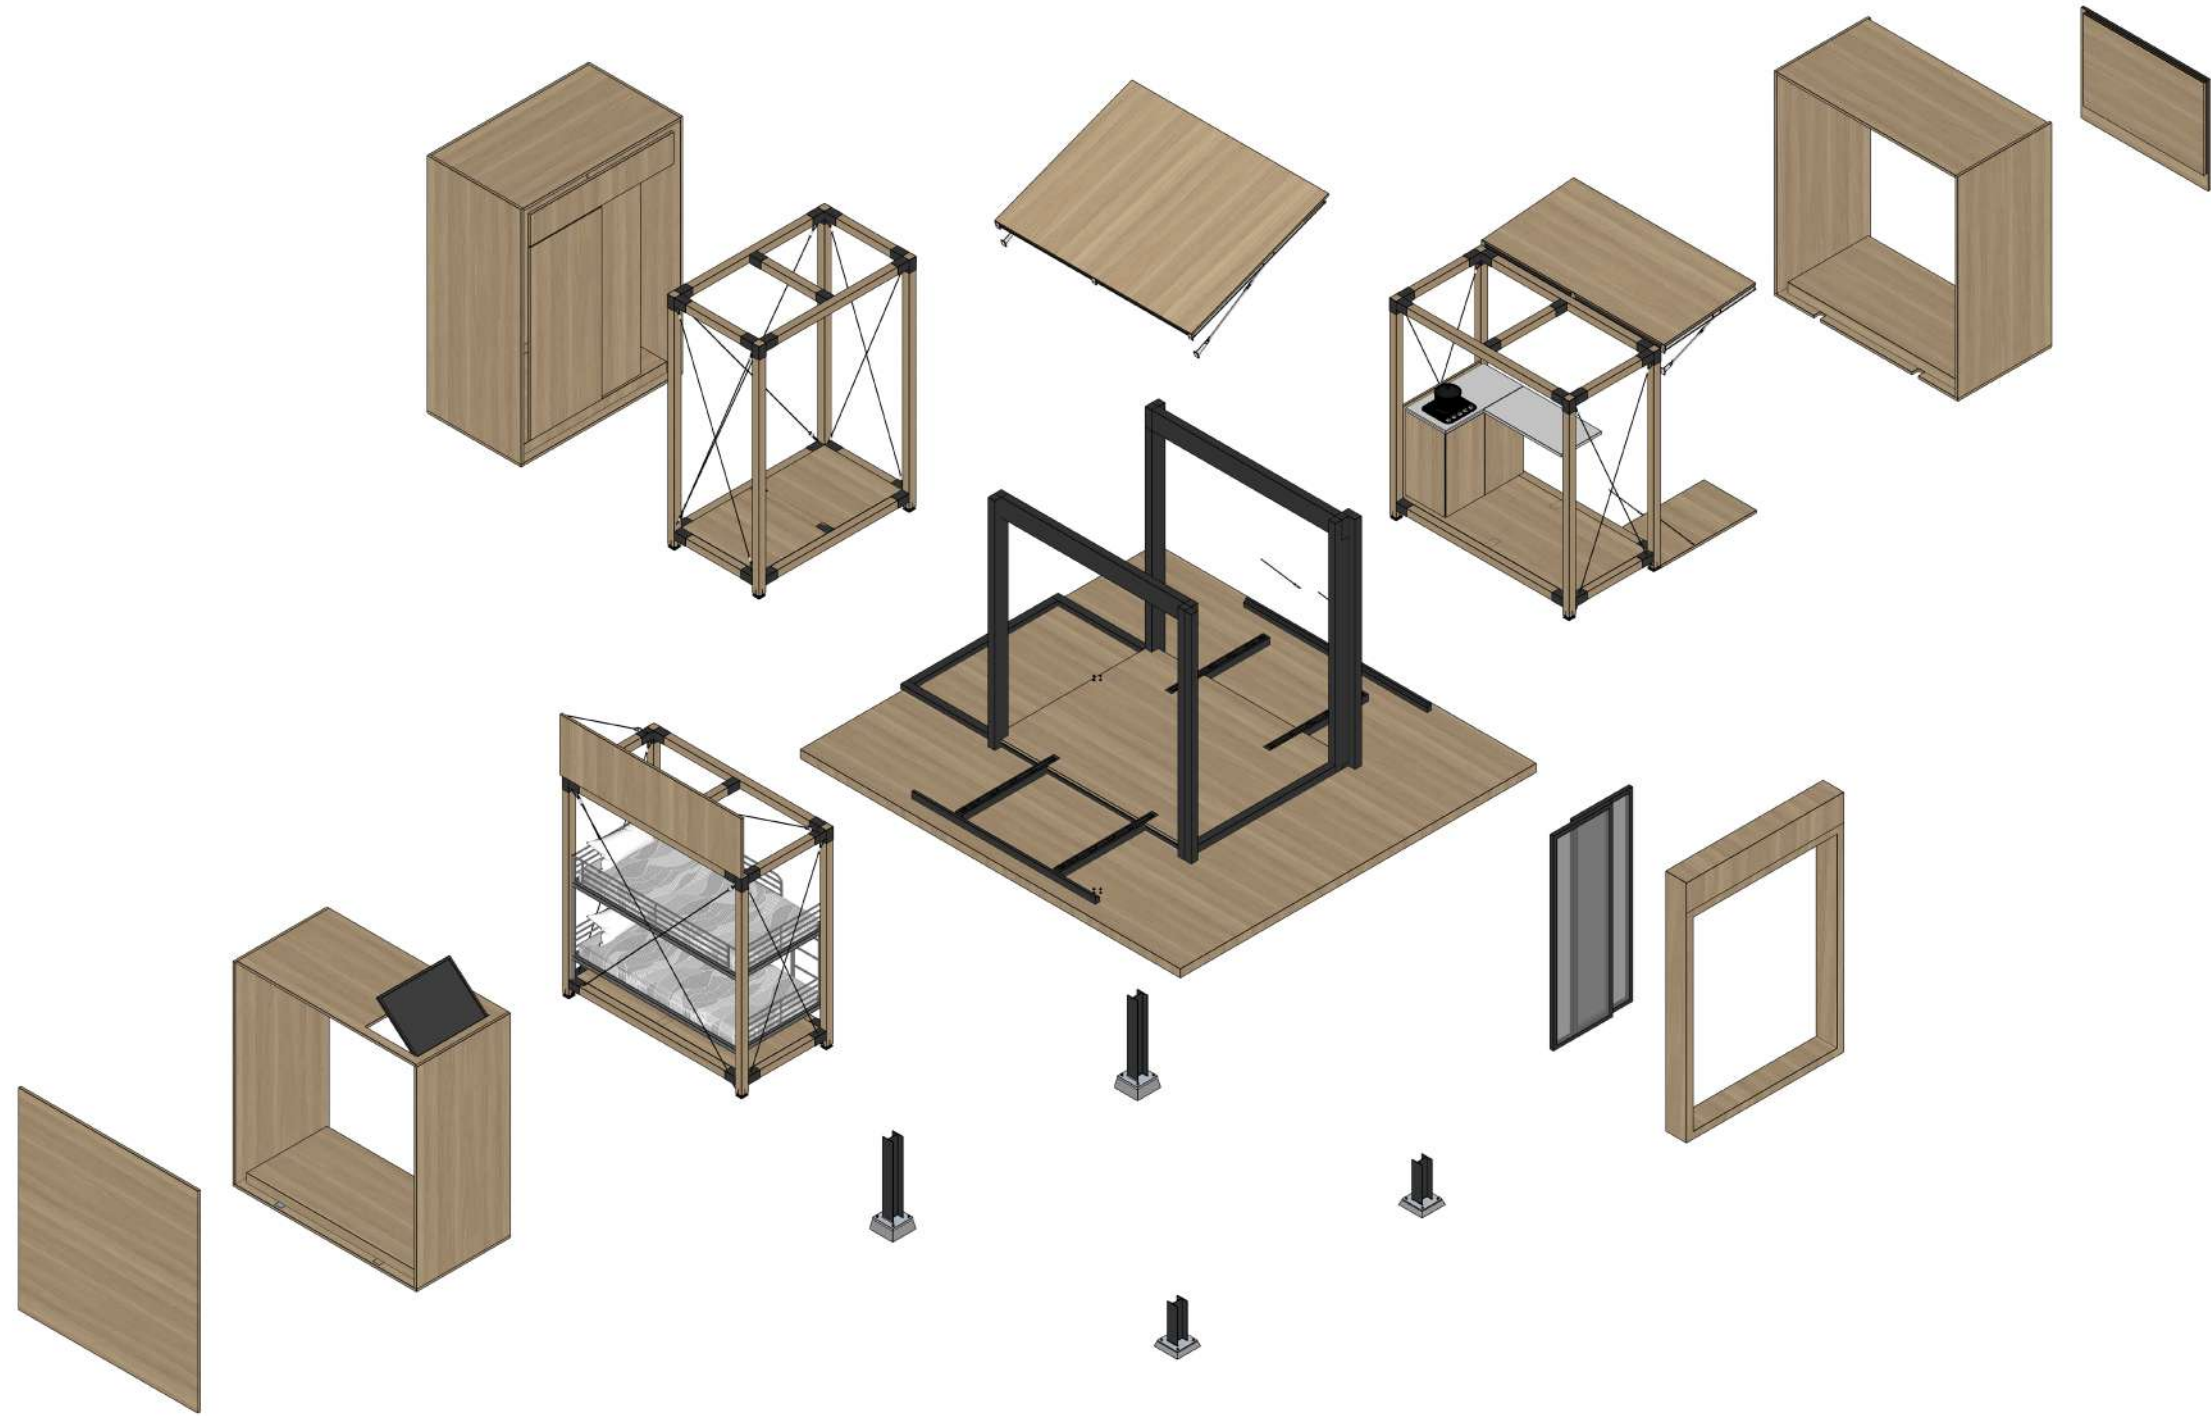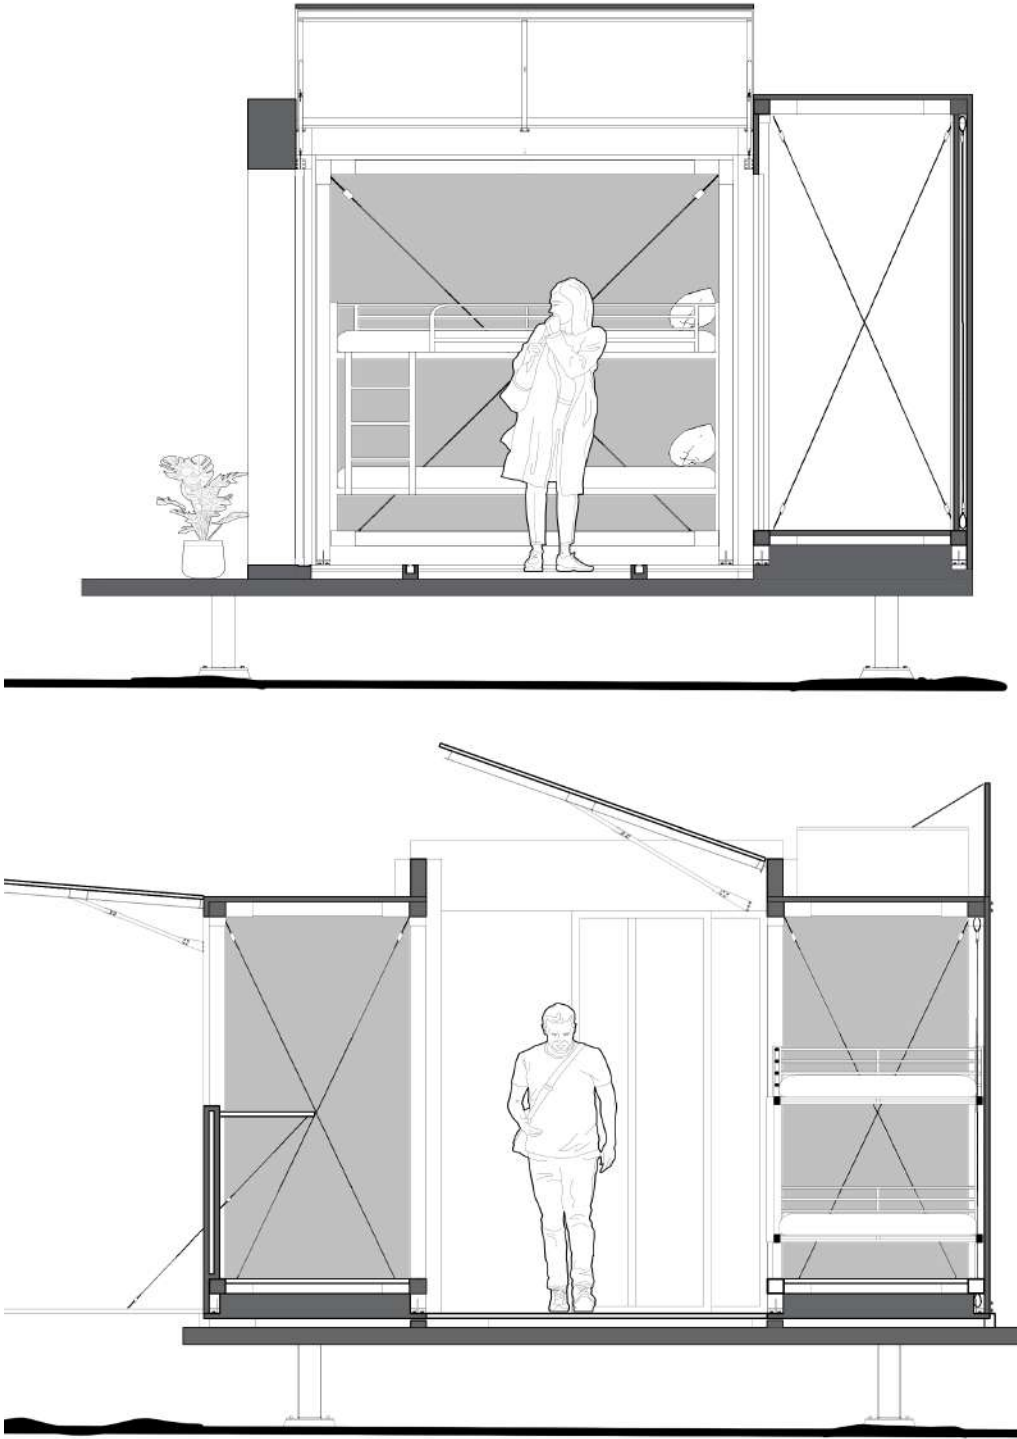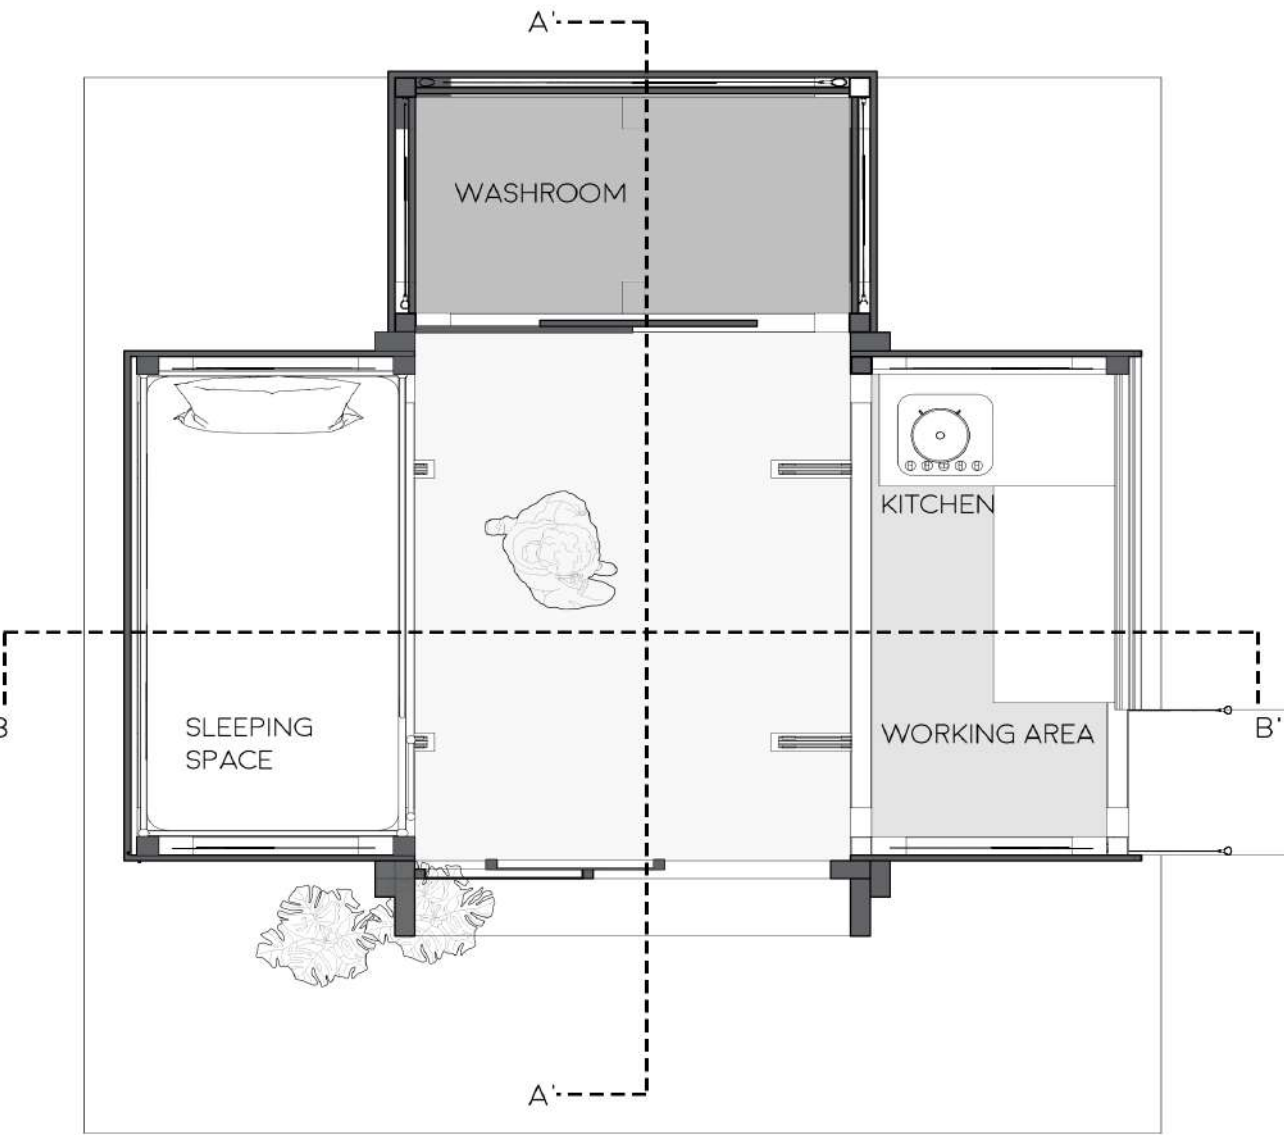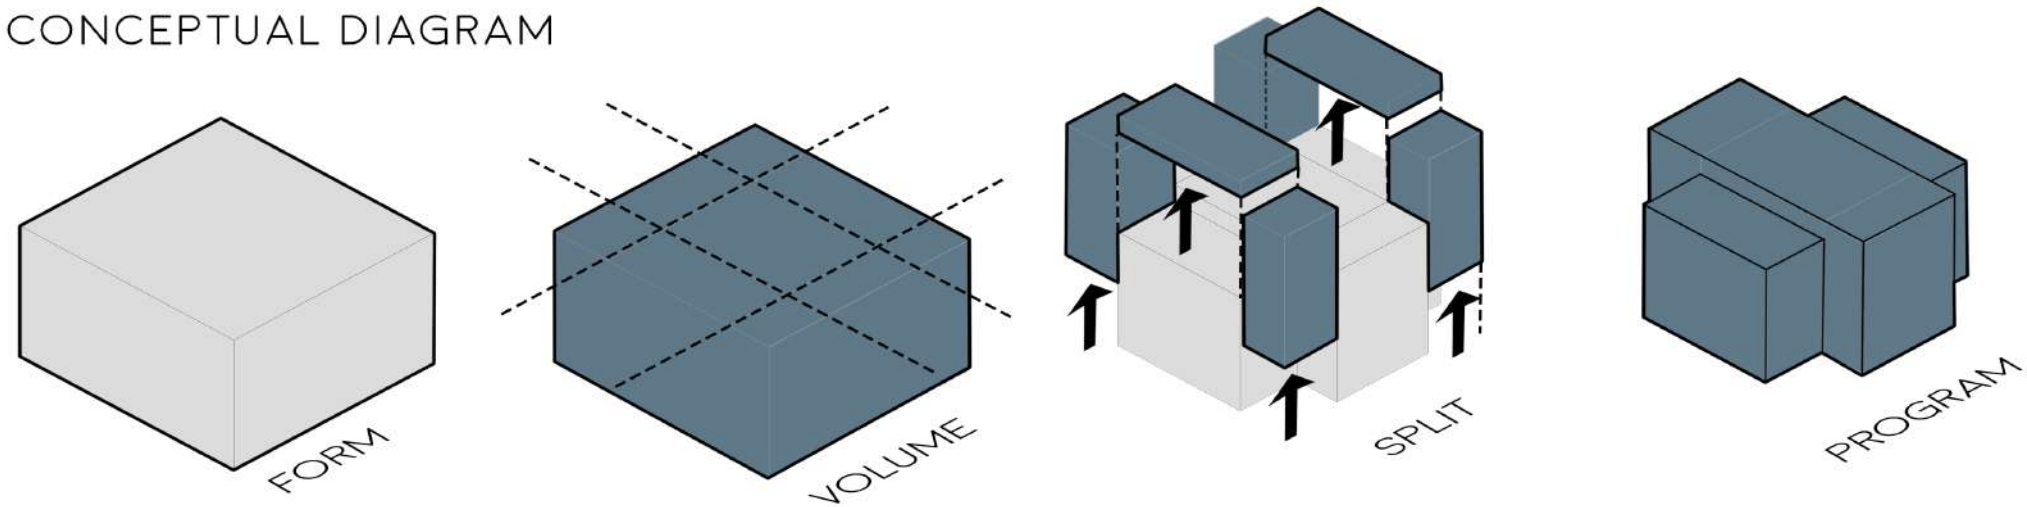

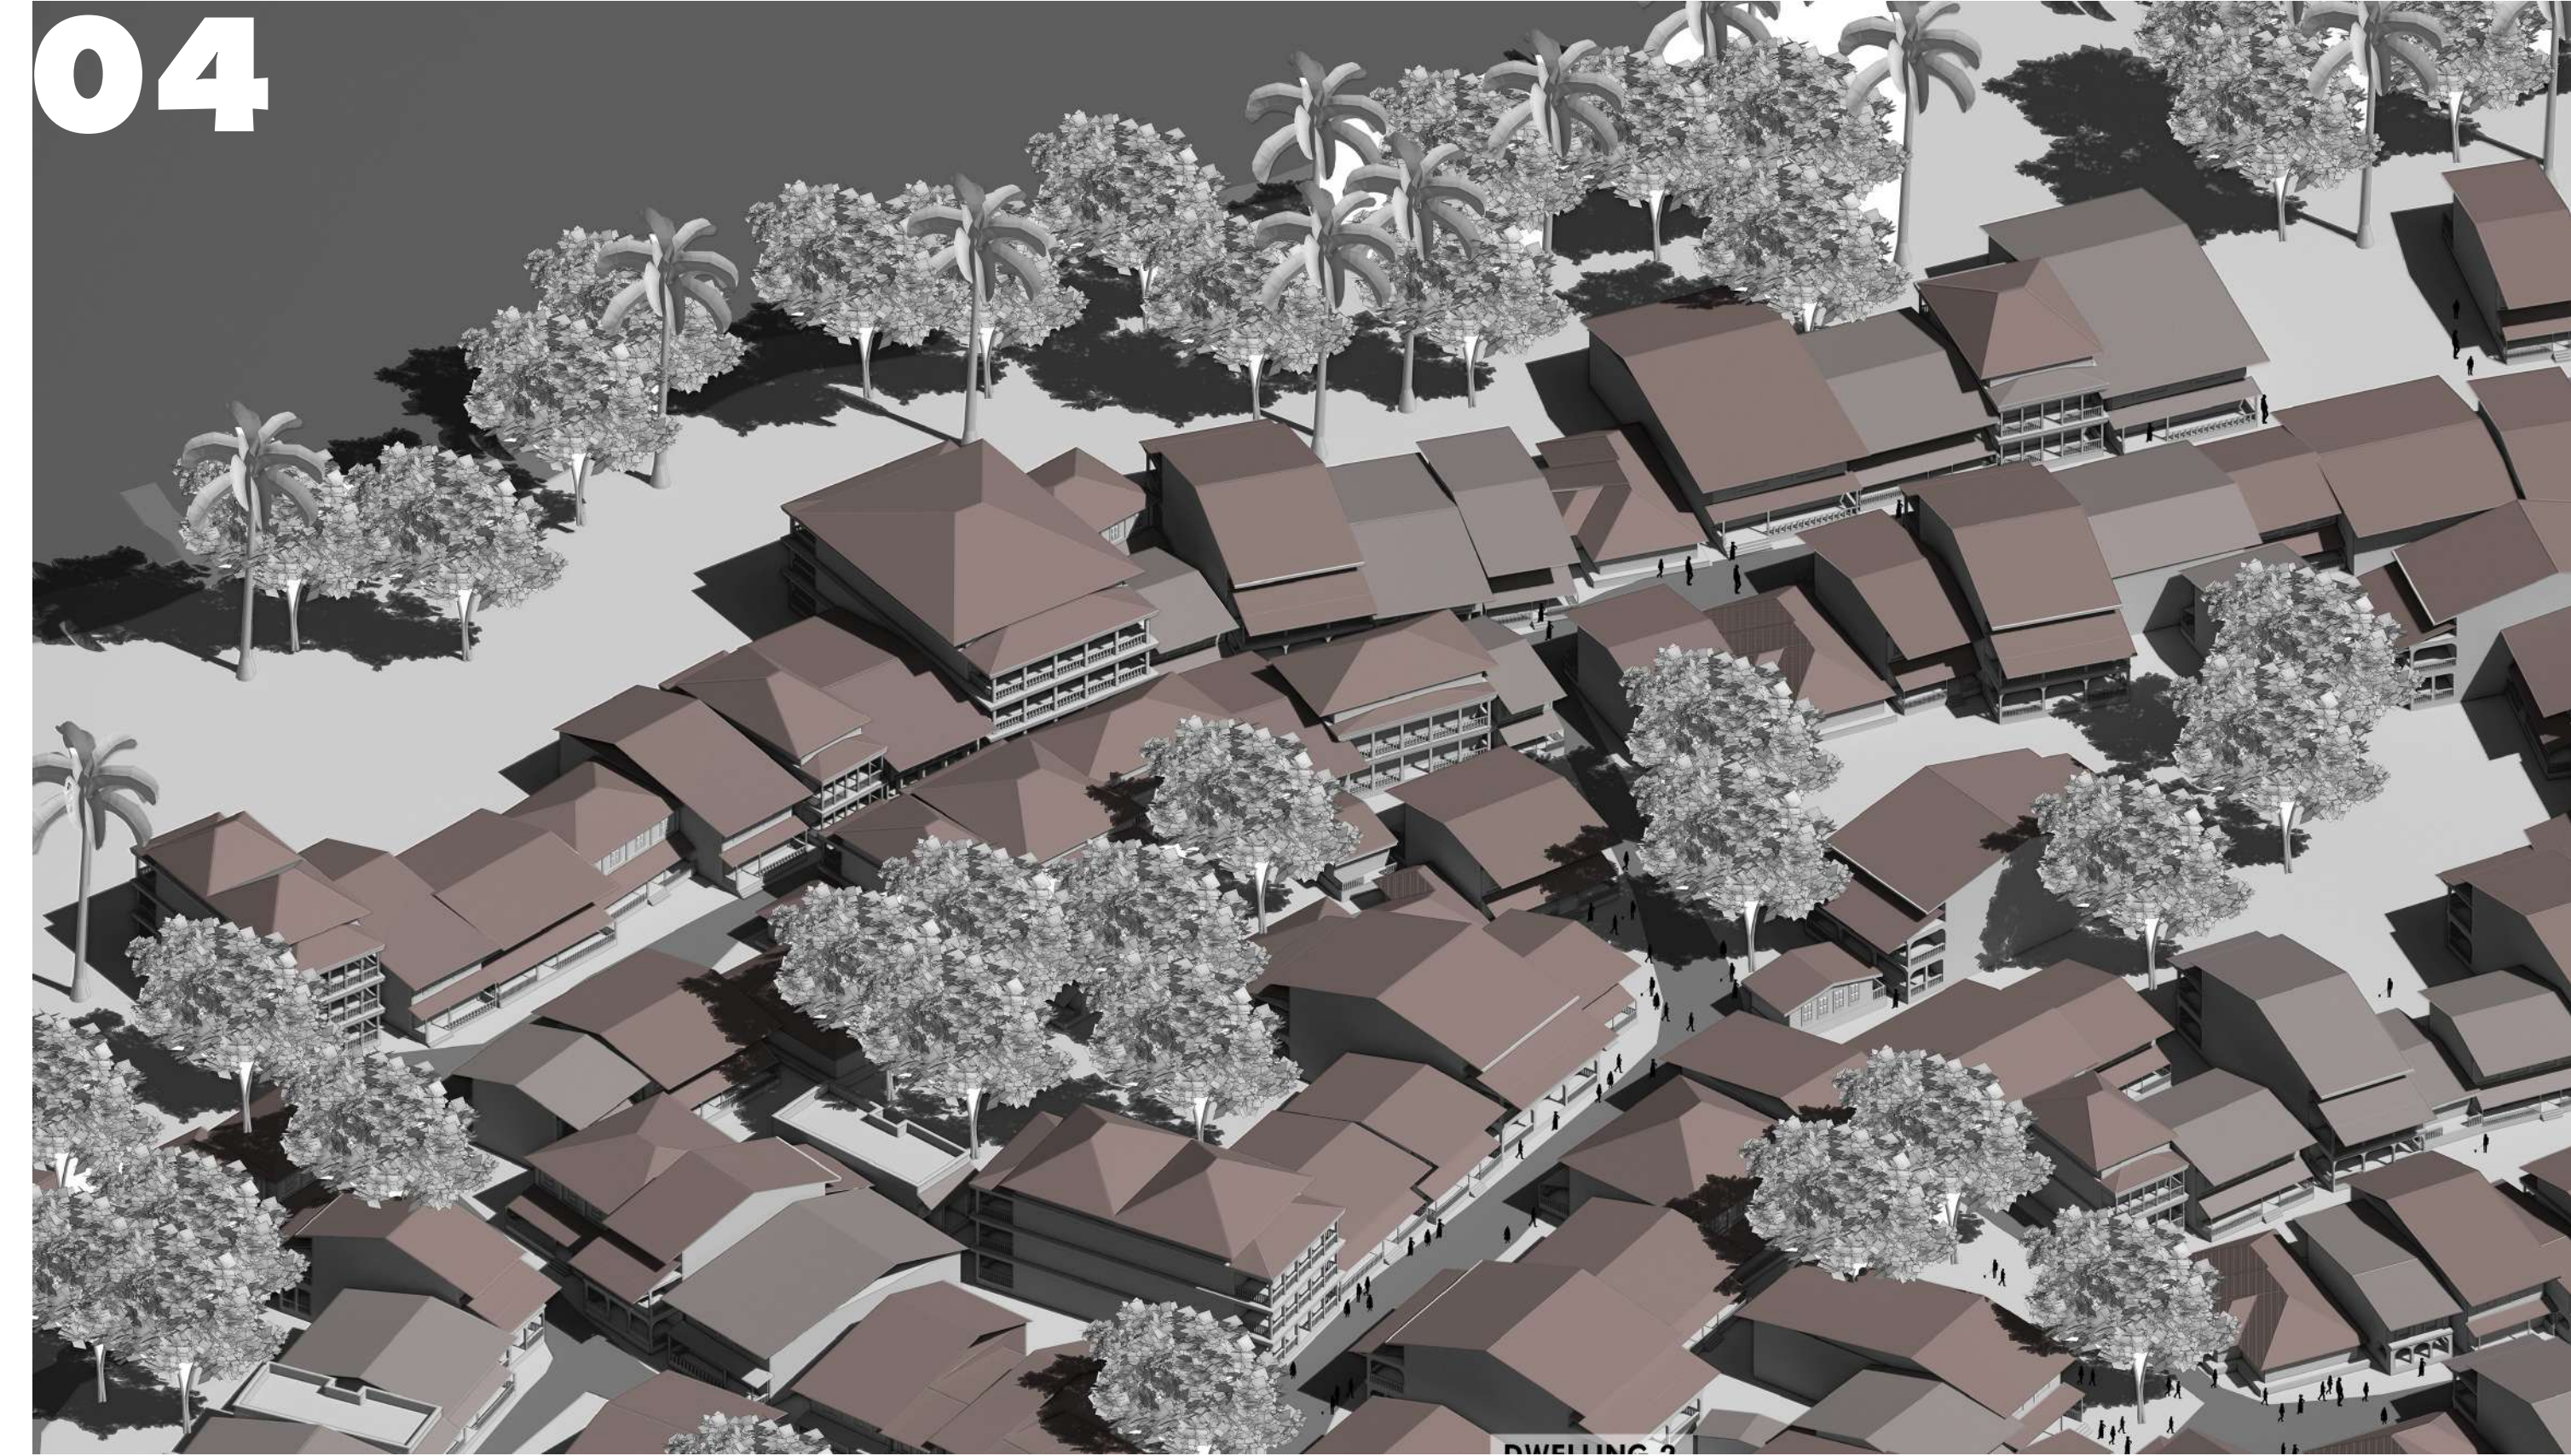

04

05 COA HERITAGE DOCUMENTATION AWARDS

THIS DOCUMENTATION OF UDVADA EXPLORES HOW ARCHITECTURE BECOMES A VESSEL OF MEMORY, FAITH, AND ADAPTATION. THROUGH THE STUDY OF INDIGENOUS PARSİ DWELLINGS, IT REVEALS A DIALOGUE BETWEEN TRADITION AND TRANSFORMATION - WHERE SPATIAL ORDER, CRAFTSMANSHIP, AND MATERIALITY NARRATE A CULTURE-S RESILIENCE. THE WORK CAPTURES UDVADA NOT MERELY AS A HISTORIC TOWN, BUT AS A LIVING TESTIMONY TO IDENTITY PRESERVED THROUGH SPACE, TIME, AND COLLECTIVE BELONGING.



